平面设计

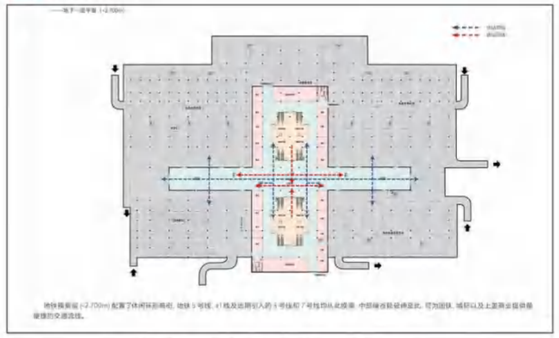

地下一层平面（-2.700m）

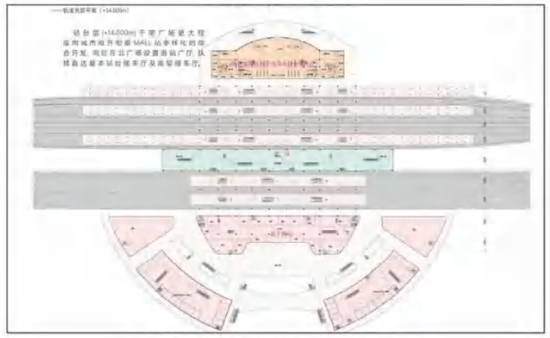

轨道夹层平面 (+14.000m)

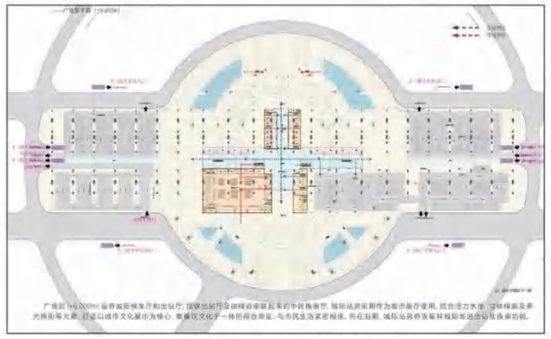

广场层平面 (+6.000m)

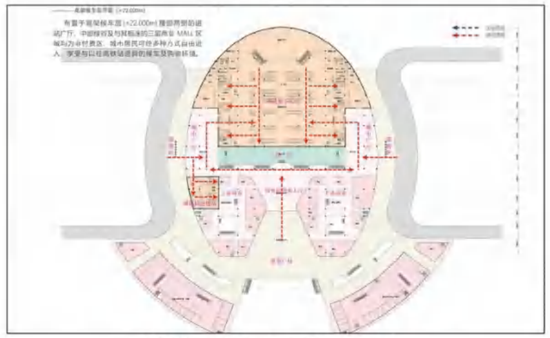

高架候车层平面 (+22.000m)

广场层平面 (+6.000m)

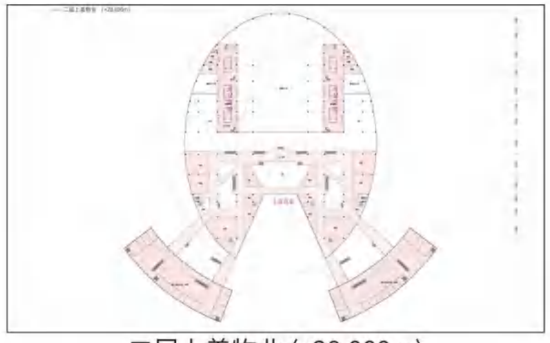

二层上盖物业 (+28.000m)

国铁候车大厅

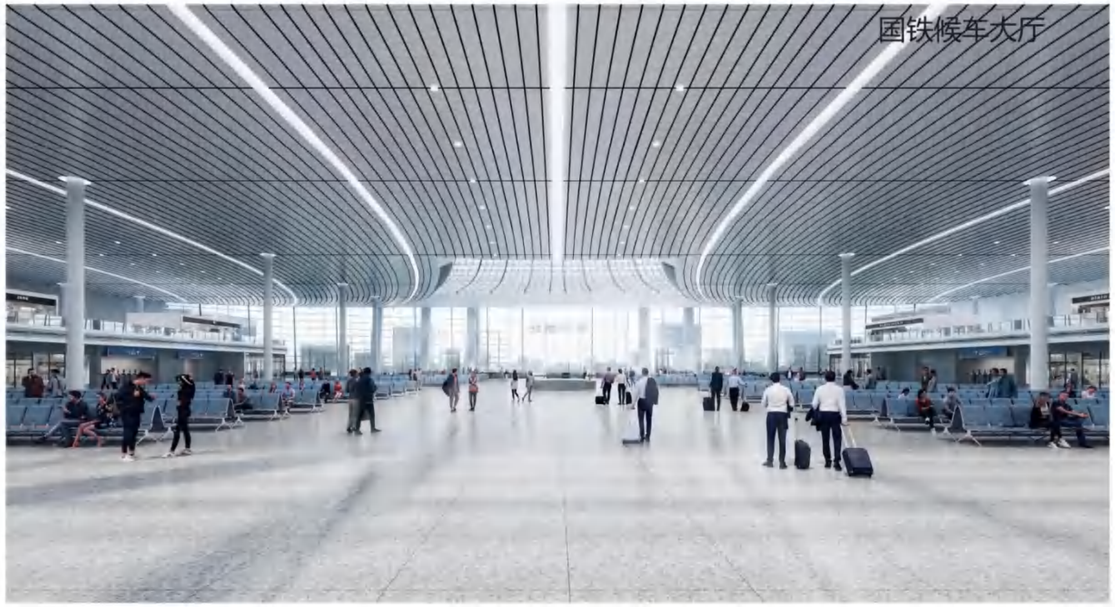
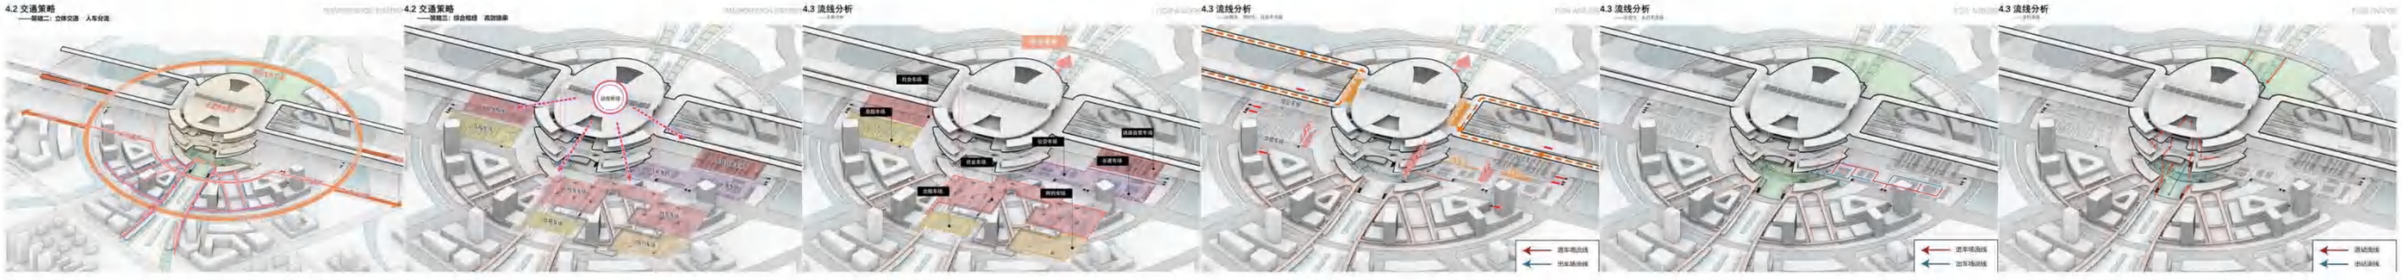
交通策略分析